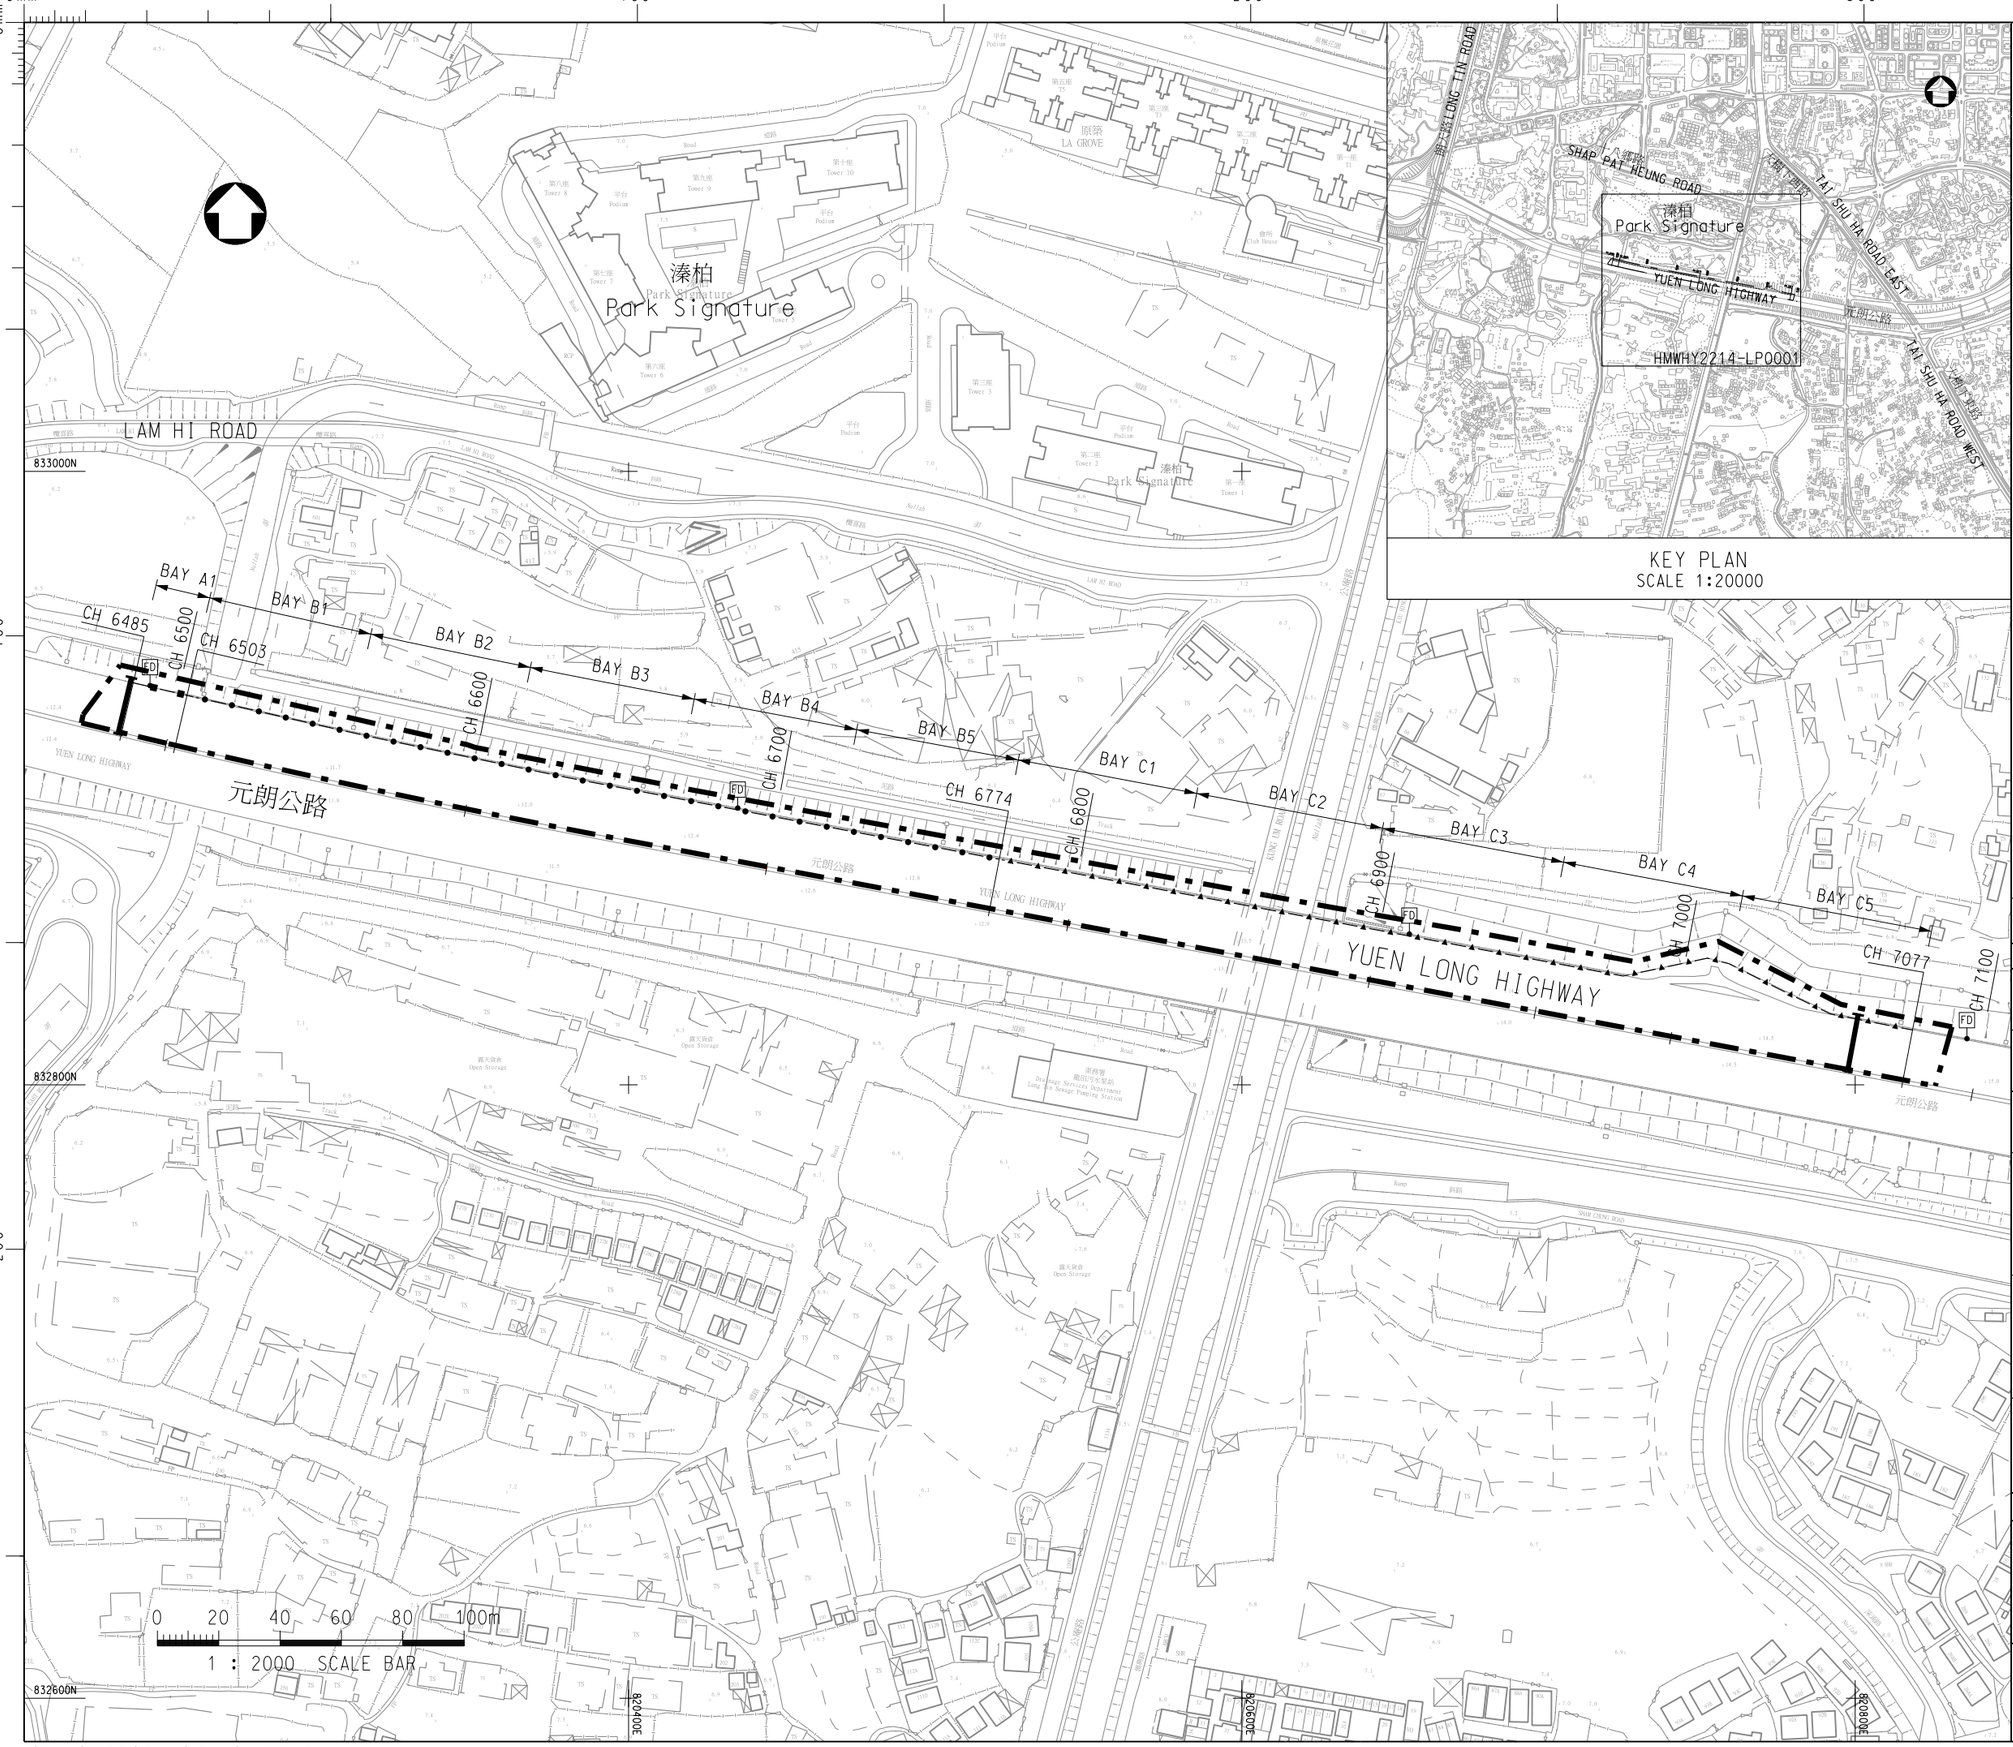

KEY PLAN
SCALE 1:20000

NOTES:

1. COORDINATES ARE RELATED TO HONG KONG METRIC GRID (1980).
2. DIMENSIONS AND CHAINAGES ARE IN METRES UNLESS OTHERWISE SHOWN.
3. THE LOCATION OF LIMIT OF WORKS SITE SHALL BE DETERMINED ON SITE AND ACCEPTANCE BY THE SUPERVISOR
4. HEIGHT OF NOISE BARRIER IS MEASURED FROM CARRIAGEWAY SURFACE.
5. FOR GENERAL NOTES, PLEASE REFER TO DRAWING NO. HMWHY2214-BH0001
6. FOR DETAILS OF TYPE D AND TYPE E NOISE BARRER, REFER DRAWING NO. HMWHY2214-BH1001 TO BH1002
7. LOCATION OF EXISTING FIRE HYDRANT, MAINTENACE DOOR AND GANTRY SHOULD BE VERIFIED ON SITE

LEGEND:

- LIMIT OF WORKS SITE
- TYPE D NOISE BARRIER TO BE MODIFIED (INCREASE BARRIER HEIGHT FROM 3.0m TO 5.0m HIGH, CHAINAGE 6485 - 6503)
- TYPE E NOISE BARRIER TO BE MODIFIED (INCREASE BARRIER HEIGHT FROM 4.0m TO 6.0m HIGH, CHAINAGE 6503 - 6774)
- TYPE D NOISE BARRIER TO BE MODIFIED (INCREASE BARRIER HEIGHT FROM 4.0m TO 5.0m HIGH, CHAINAGE 6774 - 7077)
- FD — FIRE HYDRANT AND MAINTENANCE DOOR
- GANTRY

TENDER DRAWING

no.	date	description	initial
REVISION			

designed M.T.FUNG SIGNED 31/08/22	drawn C.W.LIU SIGNED 31/08/22
checked K.L.FONG SIGNED 31/08/22	approved C.W.CHAN SIGNED 31/08/22

contract no. HY/2022/14

contract

MODIFICATION WORKS OF NOISE BARRIERS ALONG YUEN LONG HIGHWAY NEAR PARK SIGNATURE

drawing title

NOISE BARRIER LOCATION PLAN AND GENERAL LAYOUT PLAN

drawing no.	scale
HMWHY2214-LP0001	1:2000

© COPYRIGHT RESERVED

MAJOR WORKS
PROJECT MANAGEMENT OFFICE

HIGHWAYS DEPARTMENT HONG KONG

R:\Team 2\HY2214\Drawing\LP0001\HMWHY2214-LP0001.dgn

A3 420 x 297